


# PORTFOLIO

BELTRANDO ENZO • 2025

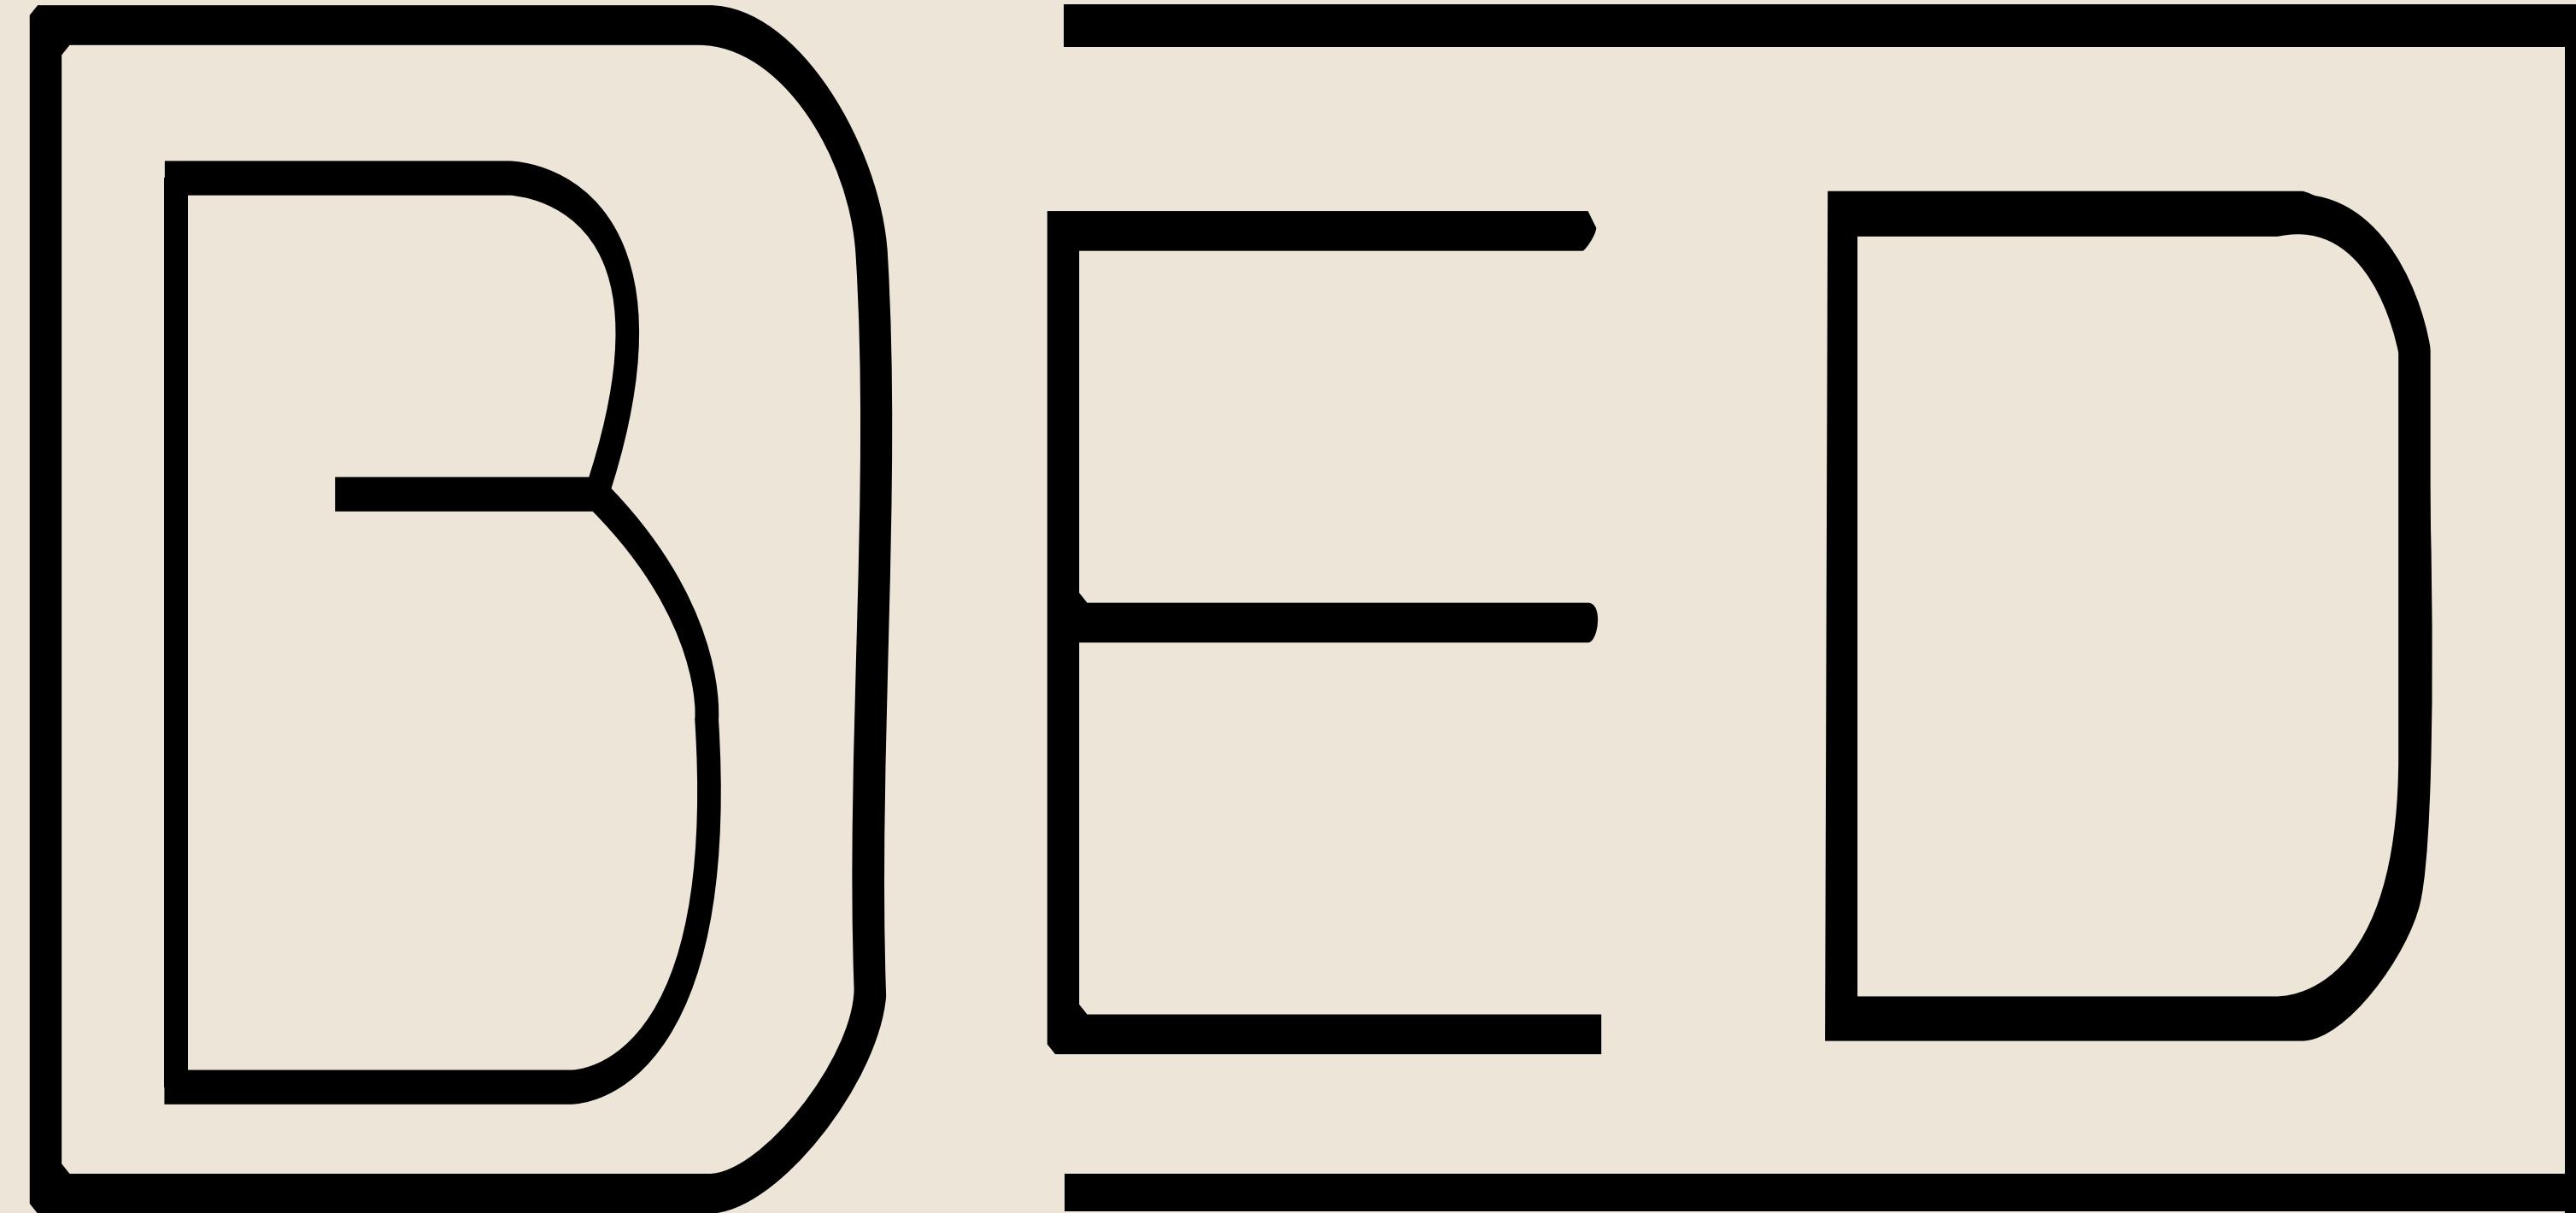

Beltrando Enzo Design



Simplicity in form, clarity in function.



# Formation

09/2023-07/2027  
Ynov Campus | Sophia

Architecture d'intérieur

09/2022-06/2023  
Seela | paris

Formation - Cyber-sécurité



09/2018- 06/2022  
Léonard de Vinci | Antibes

Baccalauréat professionnel - Économiste du bâtiment

# Hard skills



Capable de m'adapter à tout type de logiciel, je suis passionné par l'apprentissage et la compréhension de nouvelles compétences, et je considère l'échec comme une opportunité d'amélioration.

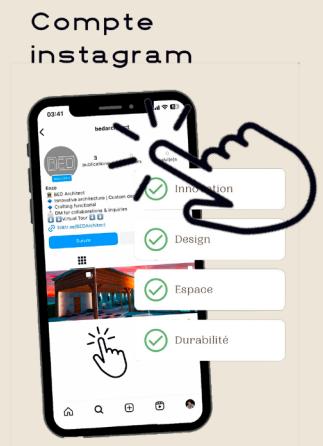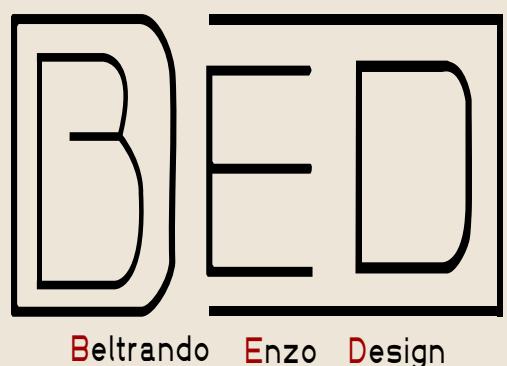

# Expérience

09/2021 - 07/2022  
Cote-d'Azur Habitat | Nice | Contrat d'alternance

Hiérarchisation des tâches afin de gérer les priorités et de respecter les objectifs de délais.

- Définition claire des problèmes rencontrés et identification des causes. Identification des difficultés et résolution des problèmes grâce à une prise de décision adaptée.

- Application des normes en vigueur, du règlement intérieur et des procédures de l'entreprise. Gestion de la documentation technique des projets DAT, DTU, plans.

- Conduite des études de faisabilité en avant-projet. Suivis, des chantiers, veillent au respect du cahier des charges et des délais de livraison.

09/2021 - 07/2022  
SEEI consultant | Vallauris | Stage

- Gestion des tâches administratives : saisie des données, classement, archivage et numérisation des documents, rédaction de compte-rendu de réunions.

- Conduite des recherches et des analyses pour soutenir les projets de l'équipe. Sur l'expérience du terrain et en effectuant les recherches nécessaires.

- Assistance des employés expérimentés dans leur travail quotidien.

11/2020 - 12/2020  
LIZEE | Mouans-Sartoux | Stage

- Attention particulière portée à la planification des tâches et établissement de plannings.

- Proposition de solutions innovantes en s'appuyant sur l'expérience du terrain et en effectuant les recherches nécessaires.

12/2018 - 12/2018  
ABC Architecte | Villeneuve-Loubet | Stage

2024/2025  
Archiproduct | AMBASSADEUR

- Représentation de la marque : J'ai agi en tant qu'ambassadeur de la marque, promouvant les valeurs et les produits

- Création de fiches techniques : J'ai élaboré des fiches techniques détaillées pour chaque matériau, incluant des spécifications, des applications, et des recommandations d'utilisation, afin d'informer et de guider les clients dans leur choix.

Doté d'un grand sens de l'organisation et d'une solide connaissance du bâtiment, je sais m'intégrer sans difficultés dans de nouveaux contextes de travail grâce à un véritable esprit d'équipe et à d'excellentes capacités d'écoute et de communication.

Contact : 06 88 98 96 90

Mail : bed.contact.me@gmail.com



<https://linktr.ee/BEDArchitect>


## SOMMAIRE



L'Écrin d'Hestia



Le Zéphir

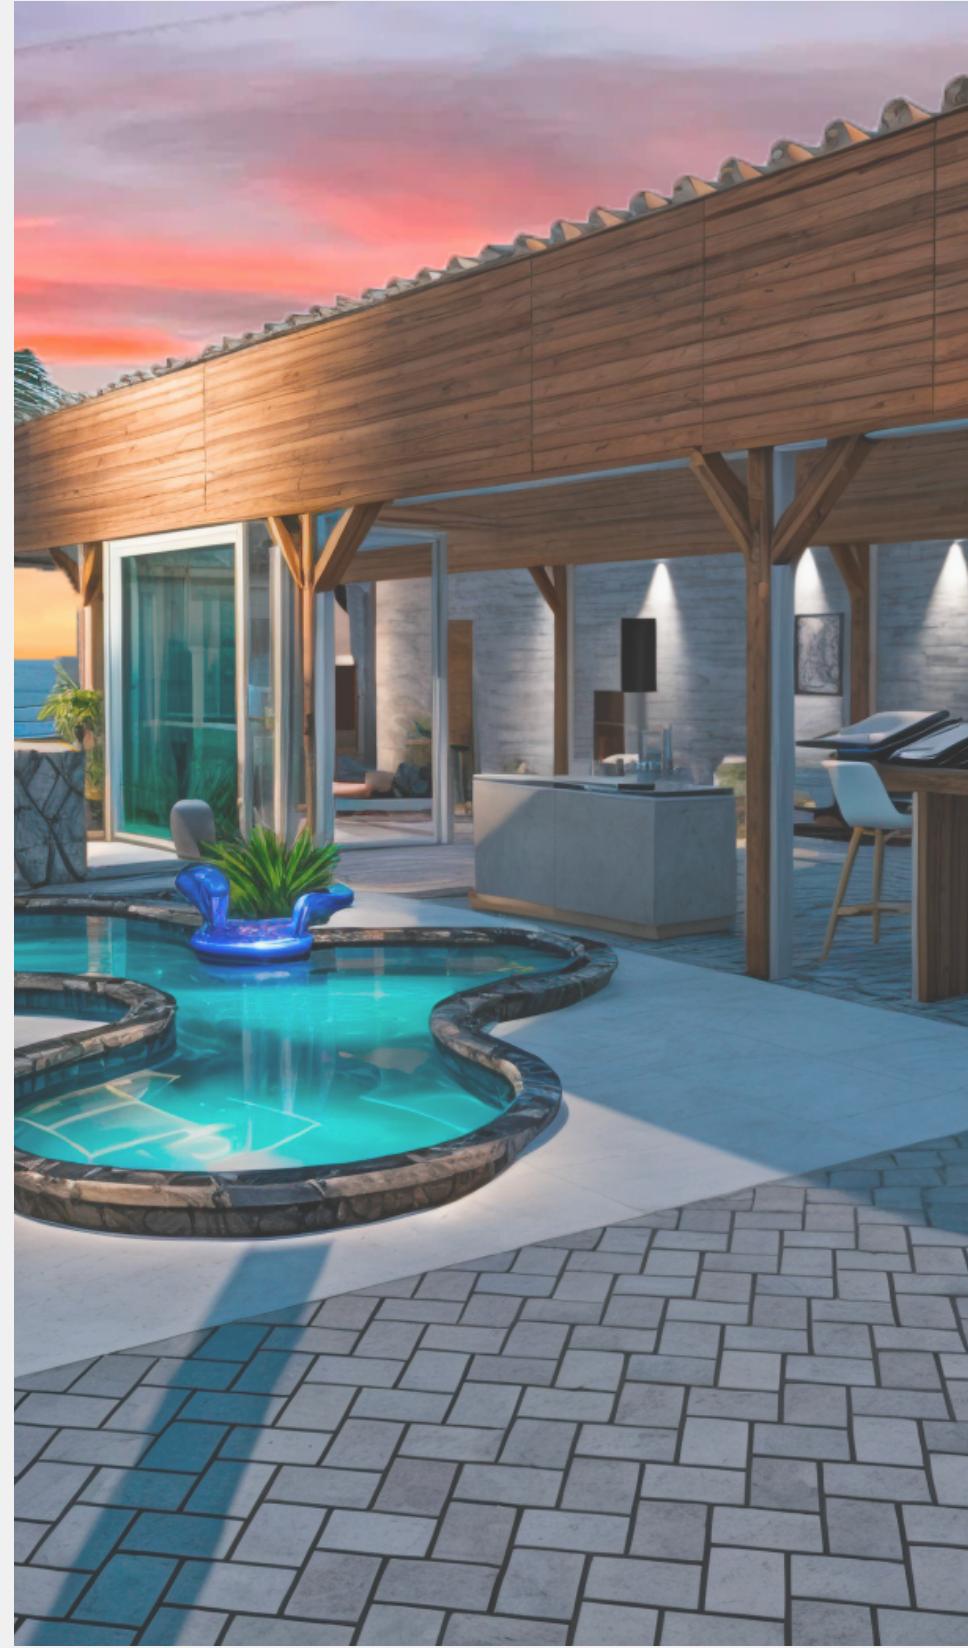

Roccia



Alma

# 01. L'Écrin d'Hestia


Ce projet de 32 m<sup>2</sup> a été conçu pour répondre au défi de maximiser l'espace tout en créant un lieu à la fois fonctionnel, élégant et chaleureux. Chaque centimètre a été optimisé grâce à des solutions astucieuses et des aménagements sur-mesure, permettant de créer un environnement confortable et pratique.



**BED**

Beltrando Enzo Design


LAITON BROSSÉ  
BOUTONS & POIGNÉES  
*Or Laque*  
SOL STRATIFIÉ  
ST MACLOU  
*Marbre Blanc*

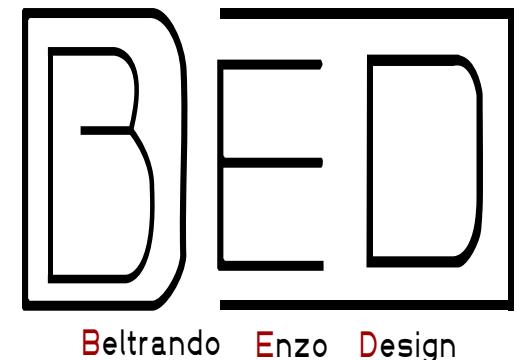

PAPIER PEINT PANORAMIQUE  
**ANANBÔ**  
*Grisaille sépia*

PARQUET CHEVRON CONTRECOLLÉ  
PARQUET-CARRELAGE.COM  
*Point de Hongrie Ongeant huilé*

TISSU BOUCLETTE  
**ASTER**  
*Karl*

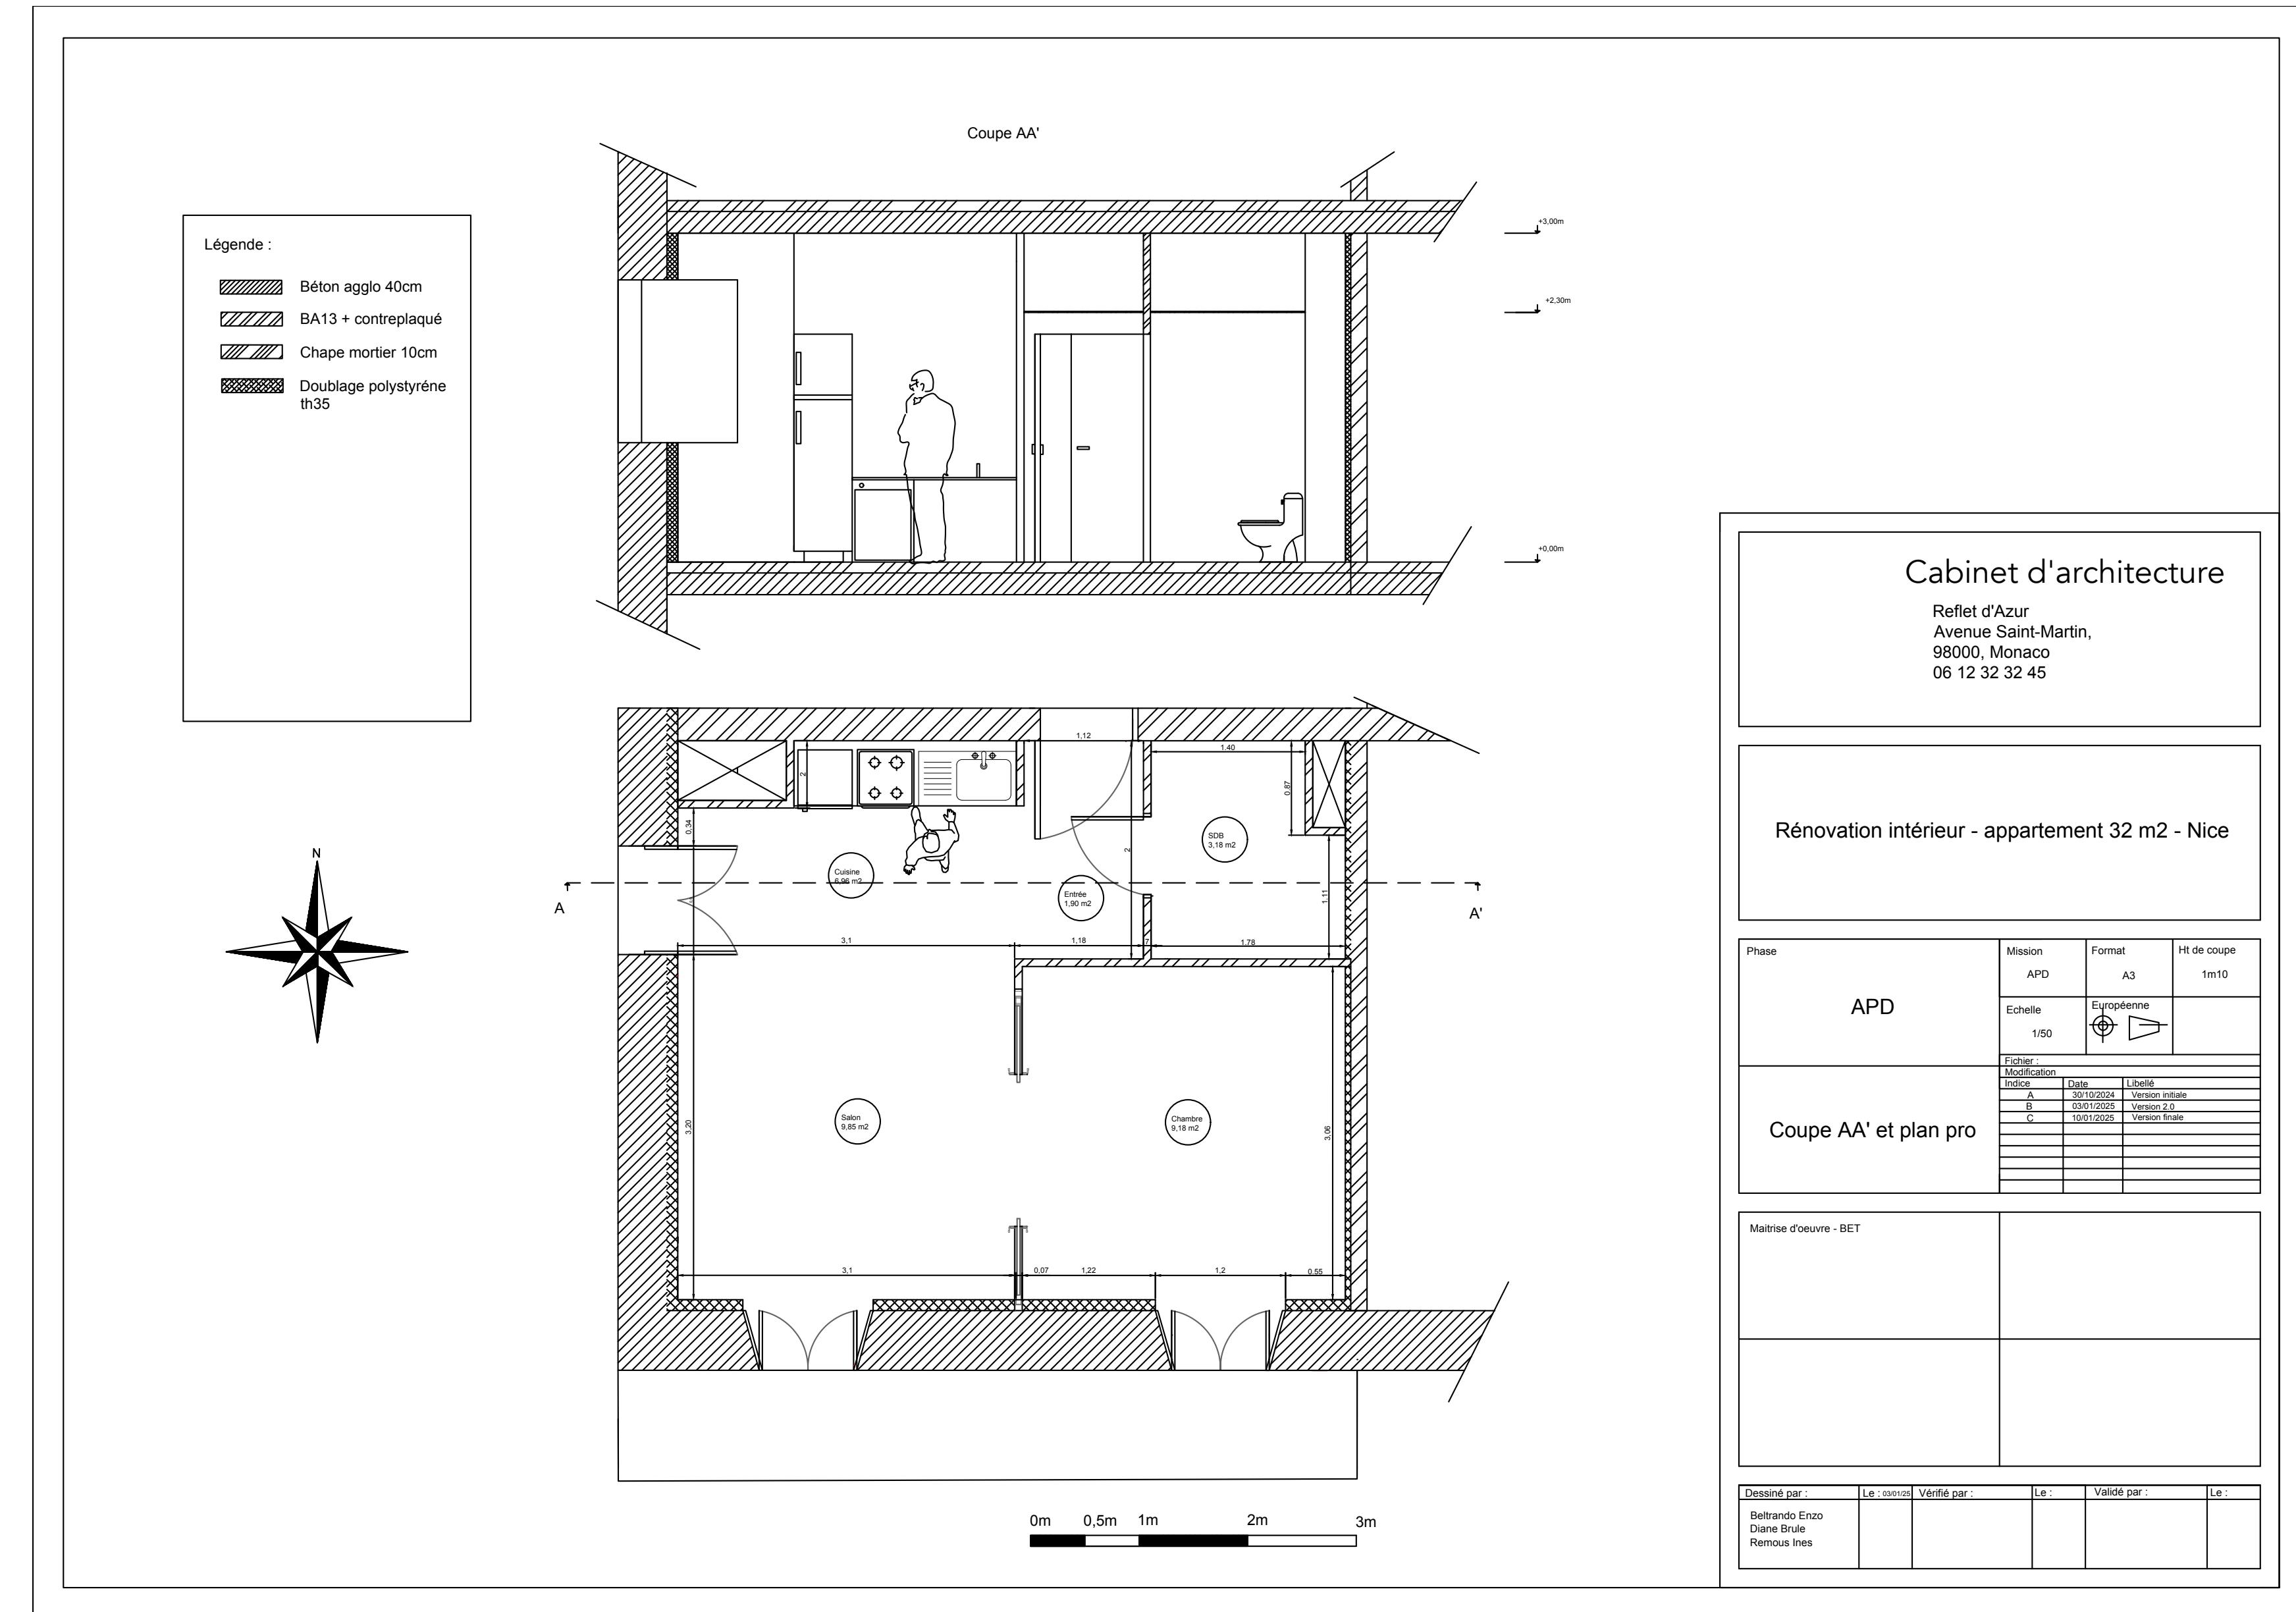

Cabinet d'architecture

Reflet d'Azur  
Avenue Saint-Martin,  
98000, Monaco  
06 12 32 32 45

Rénovation intérieur - appartement 32 m<sup>2</sup> - Nice


Phase	Mission	Format	Ht de coupe
APD	APD	A3	1m10
Echelle	Européenne 1/50		
Fichier :			
Modification			
Indice	Date	Libellé	
A	03/10/2024	Version initiale	
B	03/01/2025	Version 2.0	
C	10/01/2025	Version finale	
Coupe AA' et plan pro			

Maitrise d'œuvre - BET	

Dessiné par :	Le :	Vérifié par :	Le :	Validé par :	Le :
Beltrando Enzo Diane Brûlé Remous Ines					



## 02 Le Zéphir

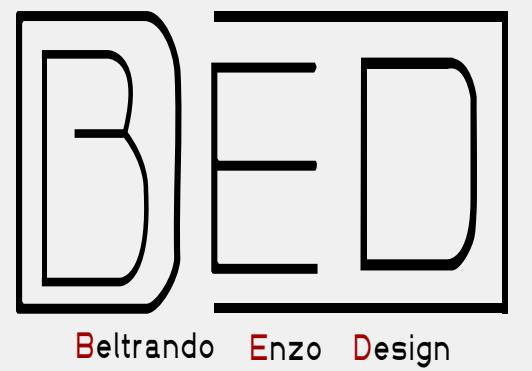


L'objectif était de concevoir un espace où l'ambiance accueillante et la circulation fluide se rencontrent harmonieusement. Chaque zone a été pensée pour favoriser une expérience agréable, du choix des matériaux à l'agencement des différentes parties du restaurant, tout en offrant un cadre propice aux échanges et à la convivialité.




BED

Beltrando Enzo Design


# Façades

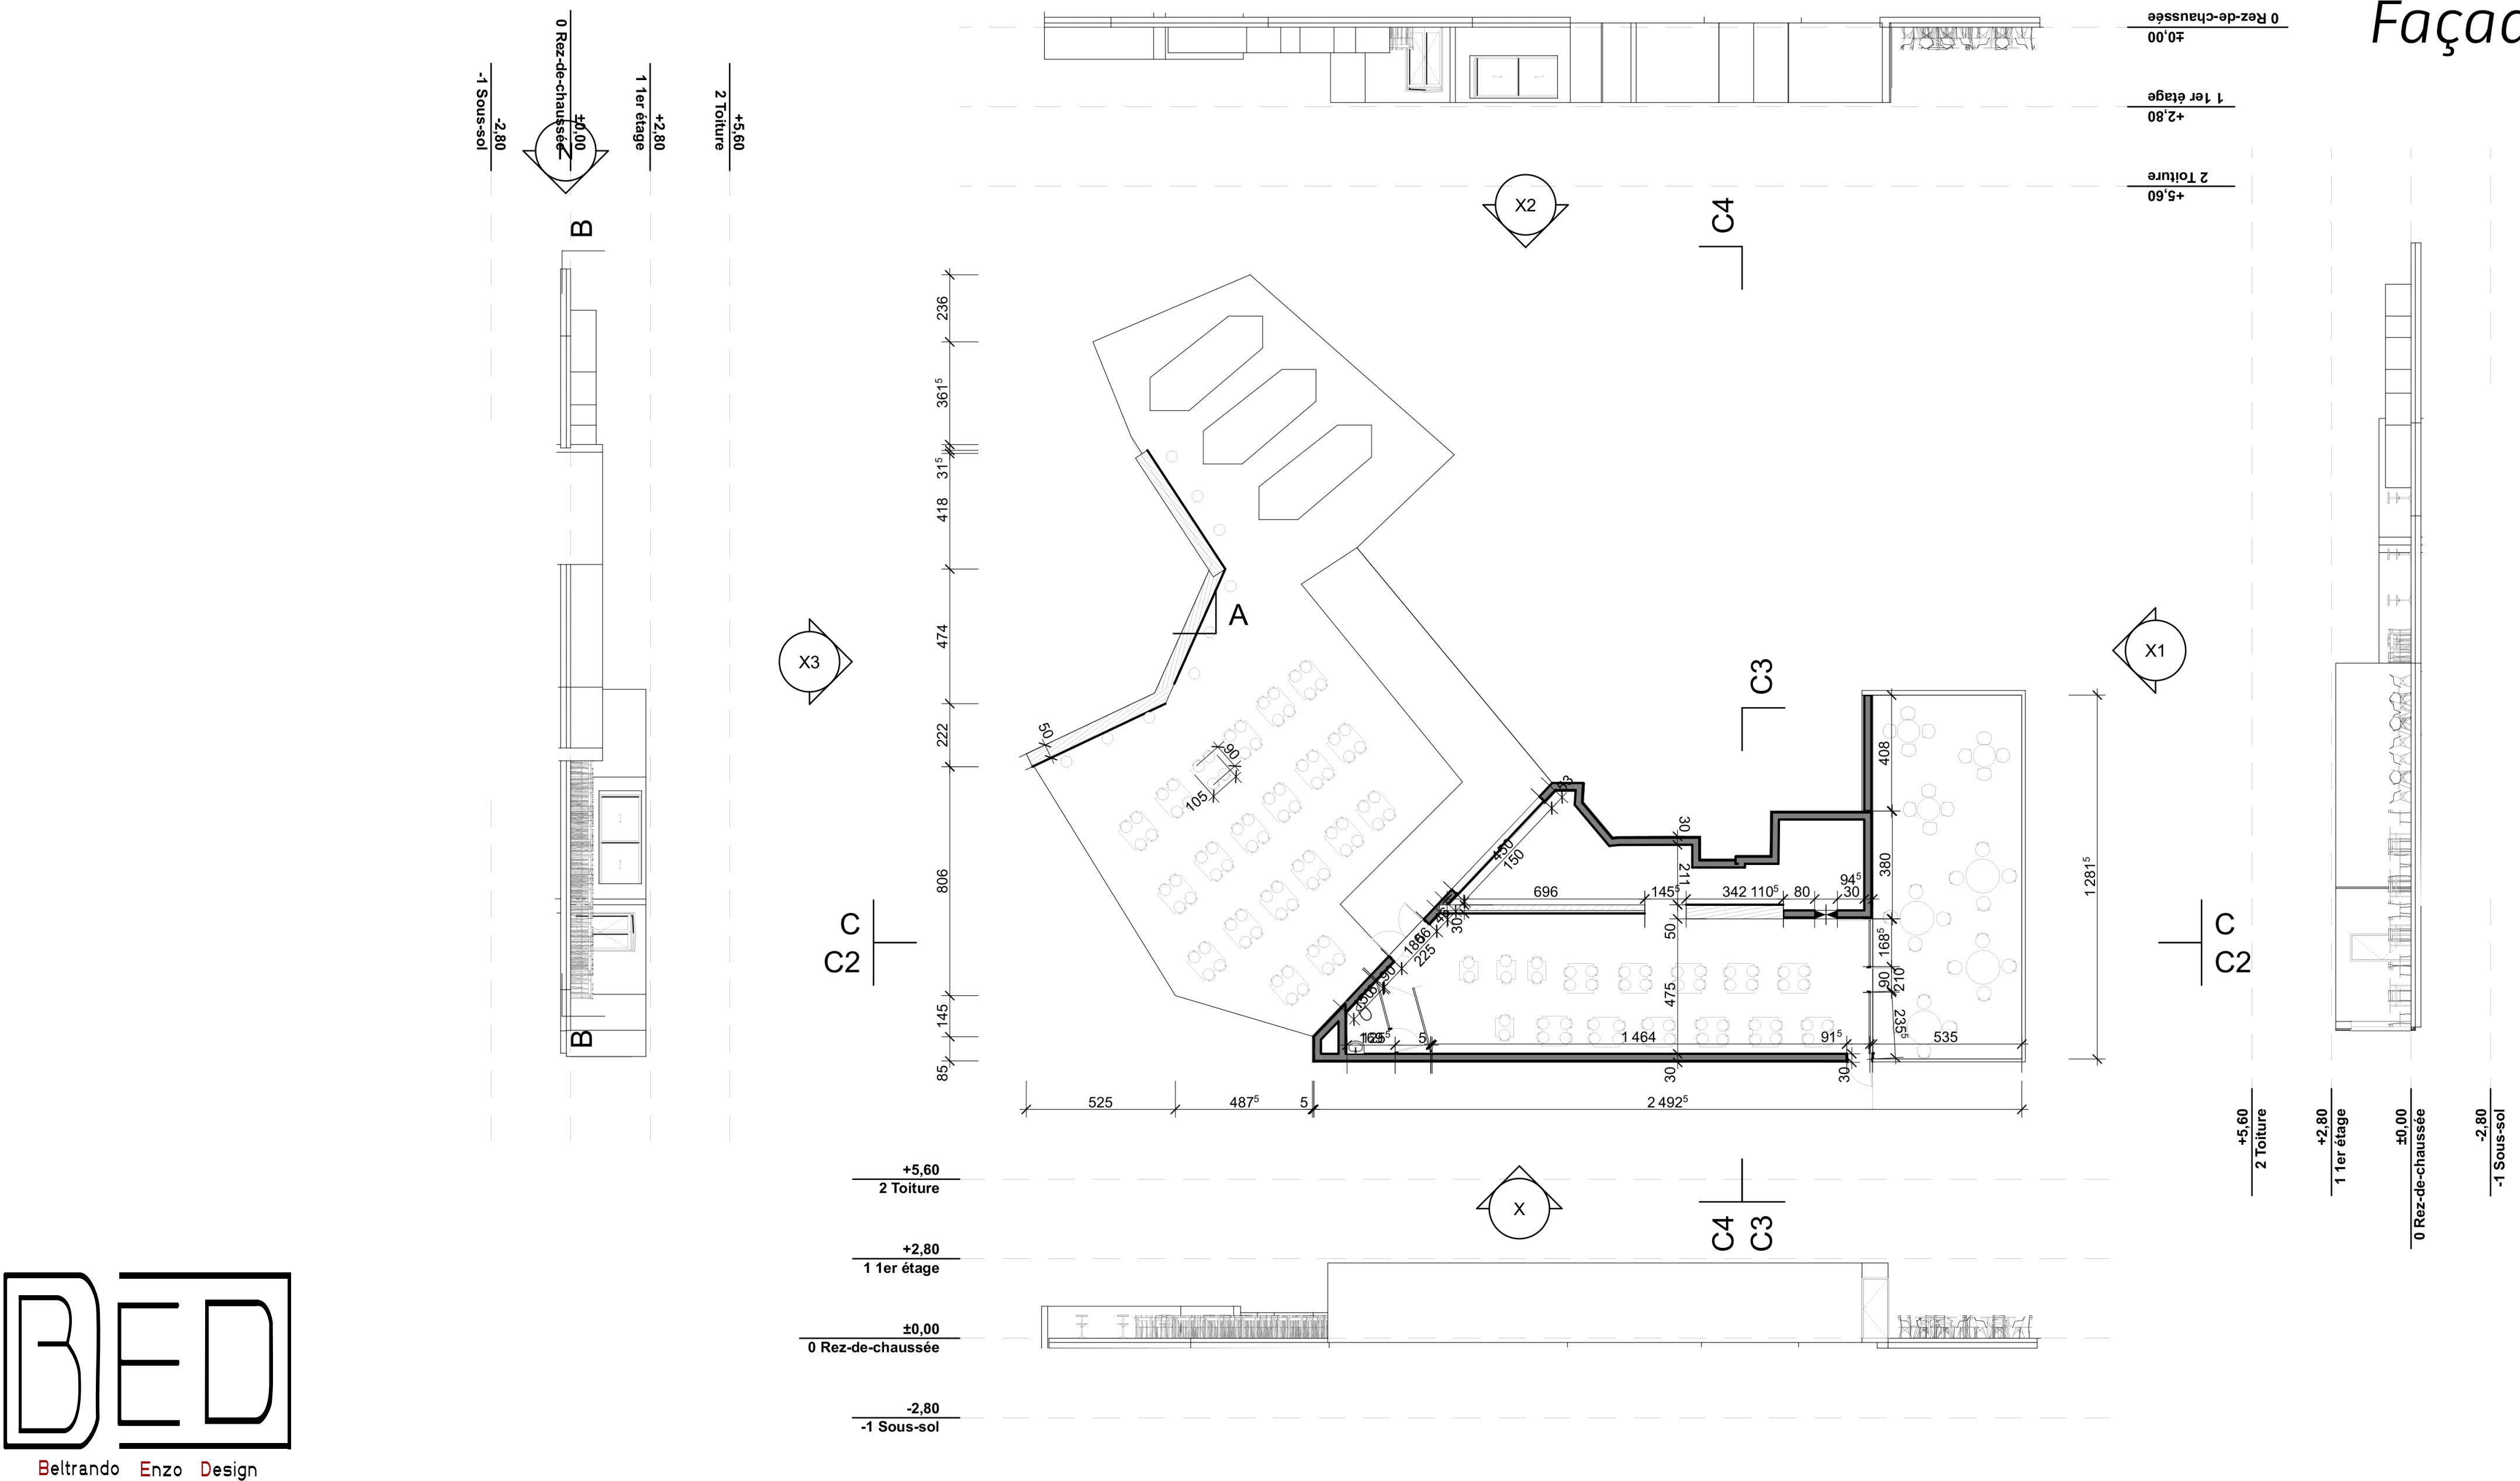

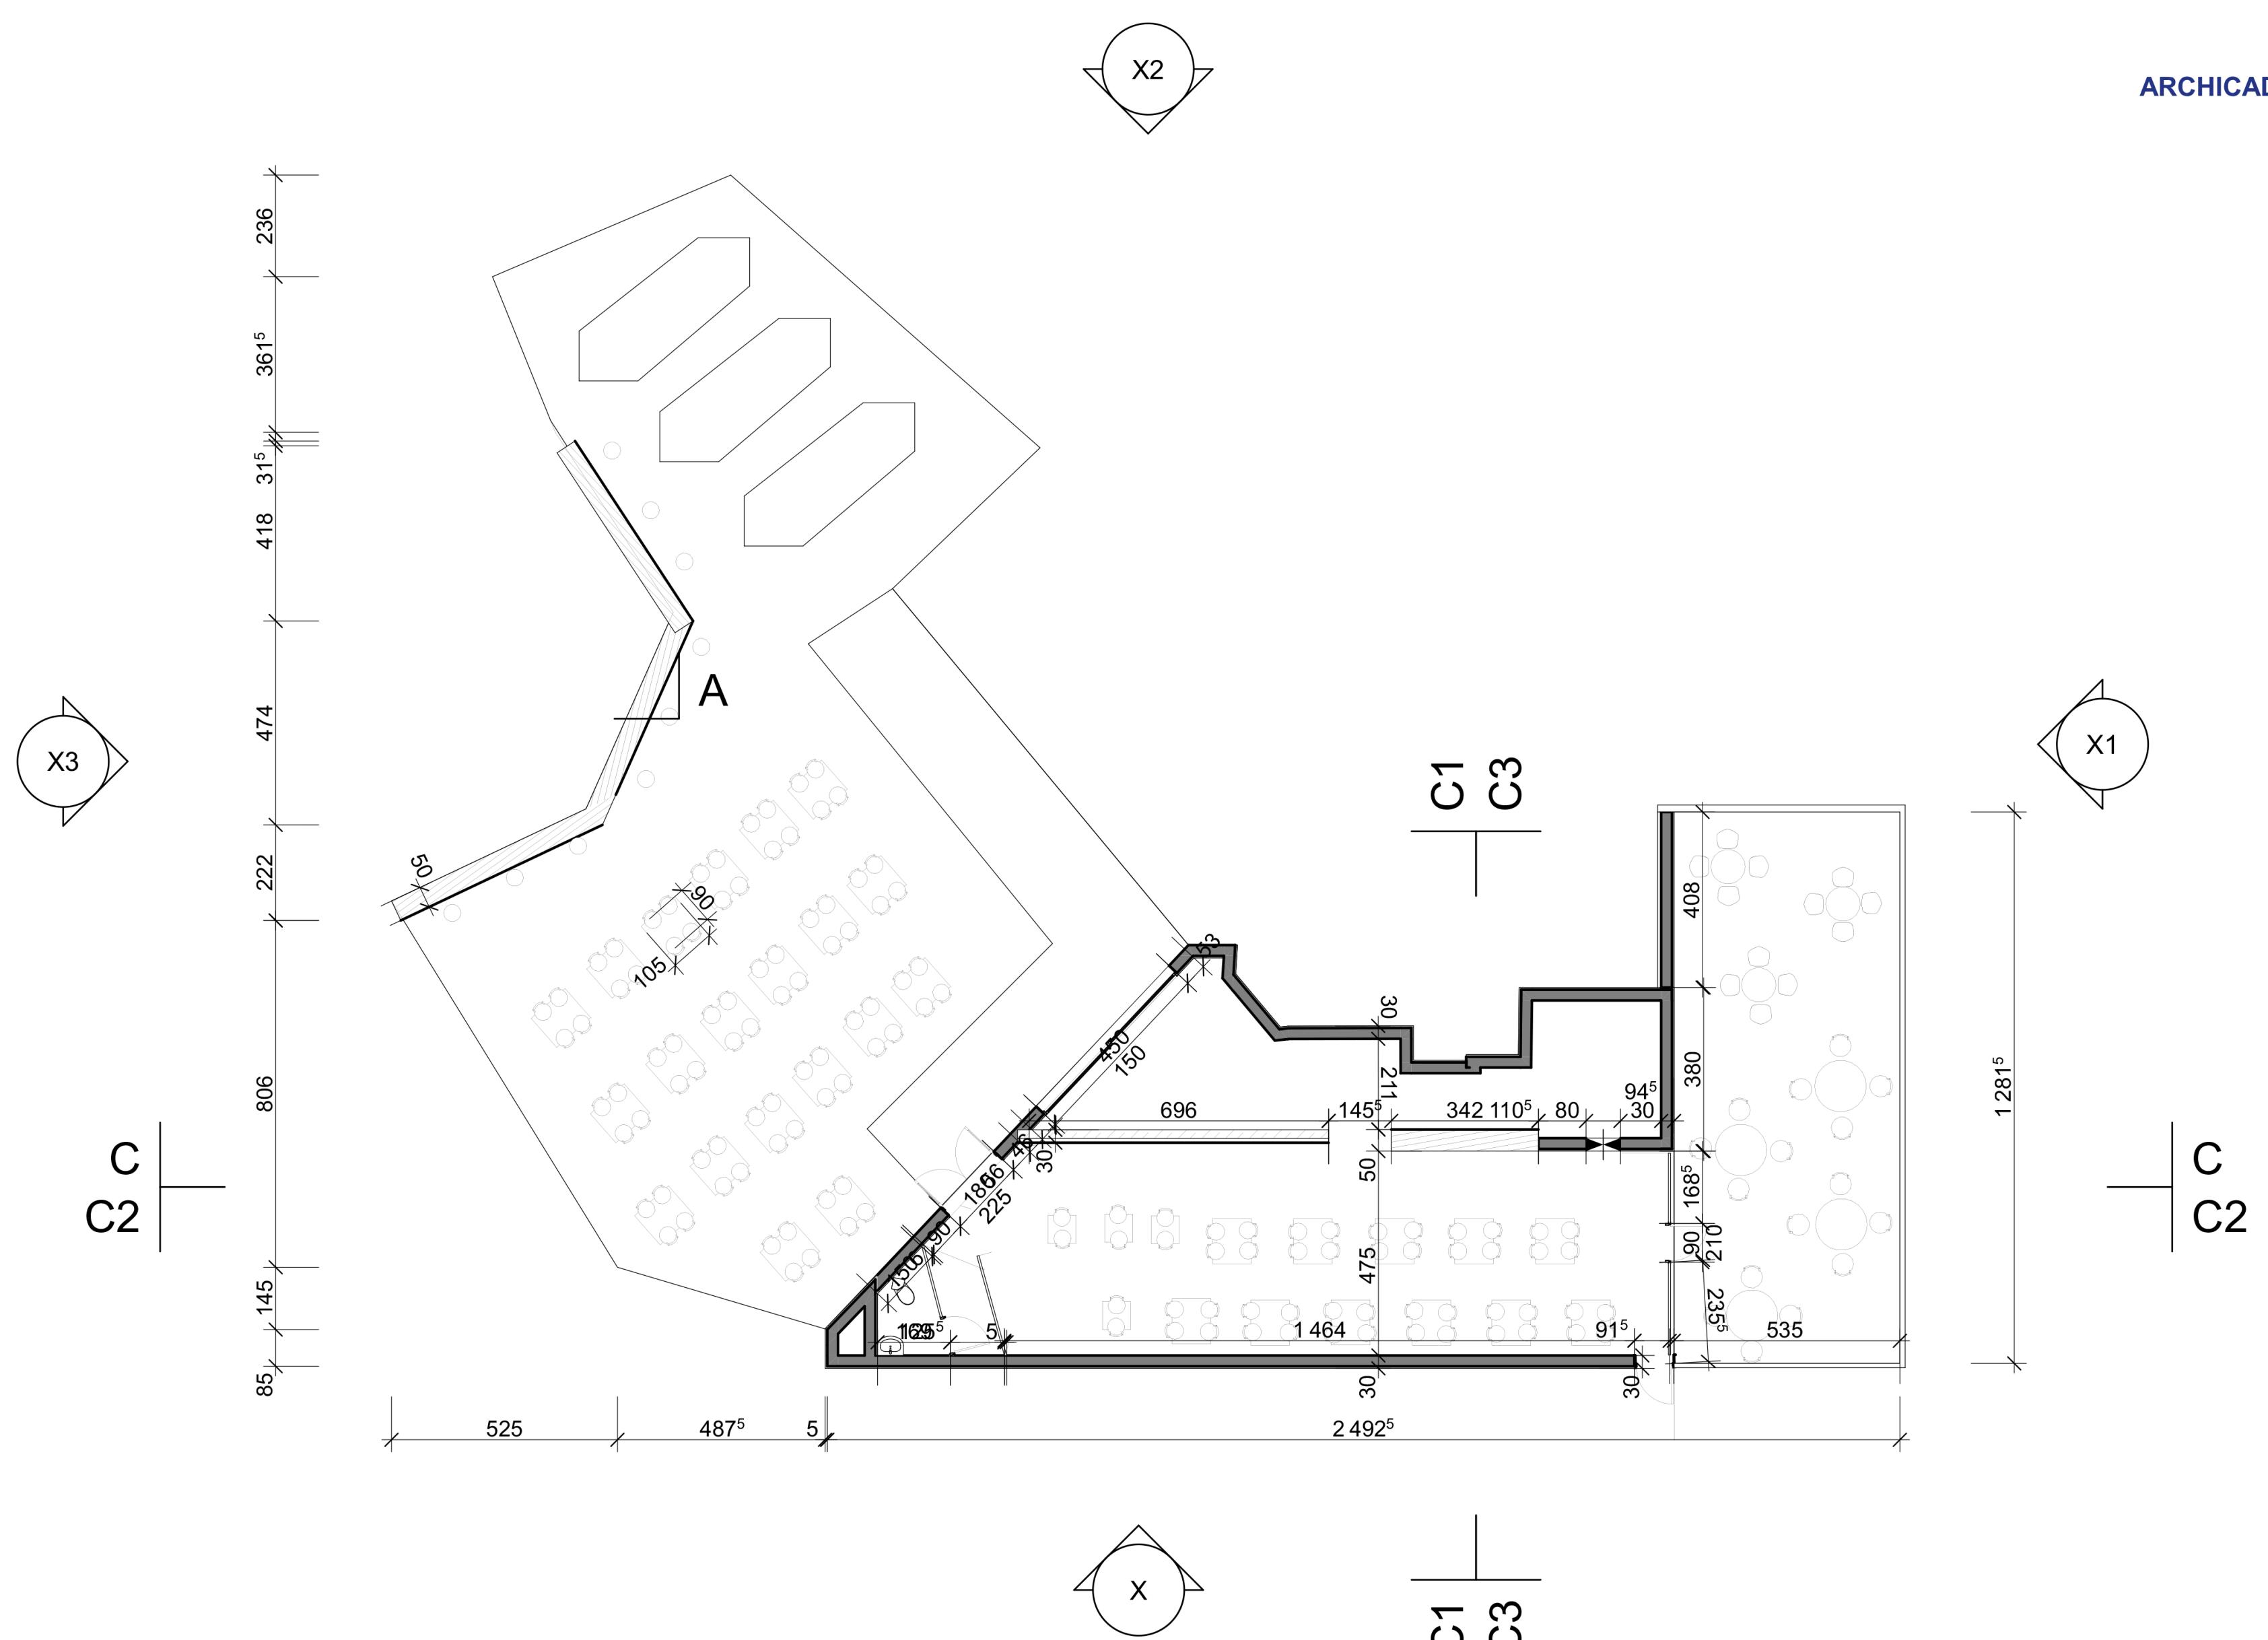


# 03 CERAZUR

Rénovation d'un espace de 100 m<sup>2</sup> pour Cerazur afin de créer une entrée de maison harmonieuse et accueillante. L'aménagement mettra en valeur les matériaux de Cerazur à travers un design esthétique et fonctionnel, offrant une expérience immersive aux visiteurs.

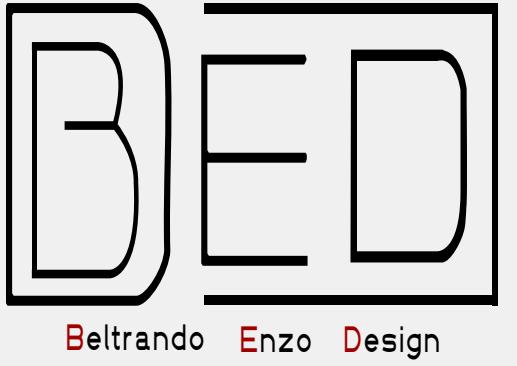

# Planche

Cette planche graphique illustre l'essence même du projet à travers une sélection soignée de matériaux, textures et couleurs. Chaque élément visuel a été choisi pour refléter l'harmonie entre l'esthétique et la fonctionnalité, tout en créant une ambiance unique.

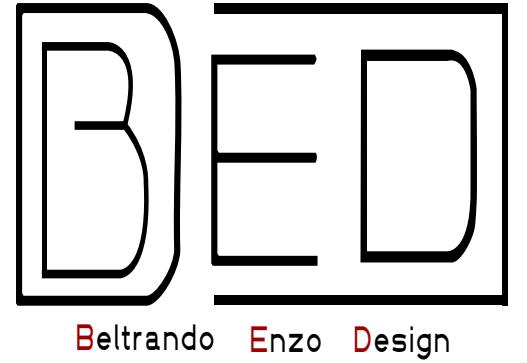

**Roccia**  
Un voyage à travers les pierres...

Roccia signifiant «roche» en italien, en lien à la fois avec les carrières et l'esthétique de jardins minéraux. Notre concept s'appuie sur les pierres naturelles provenant des carrières emblématiques d'Italie, telles que celles de Carrare, célèbres pour leur marbre de qualité exceptionnelle. Ces pierres seront mises en valeur à travers une façade de maison typiquement italienne, qui reflète l'authenticité de l'architecture méditerranéenne. Pour sublimer l'ensemble, une rosace en mosaïque sera intégrée, fusionnant l'artisanat traditionnel italien avec un design raffiné. Ce mariage entre la pureté des matériaux et l'esthétique délicate de la mosaïque crée un espace où chaque élément raconte une histoire, alliant nature et savoir-faire d'exception.

**Situation**

**Coups**

**Textures**


**3D**

**Coupe AA'**  
**Coupe BB'**  
**Coupe CC'**

**QR code**

**Visite virtuelle cliquer ici**

**VR**  
**360°**

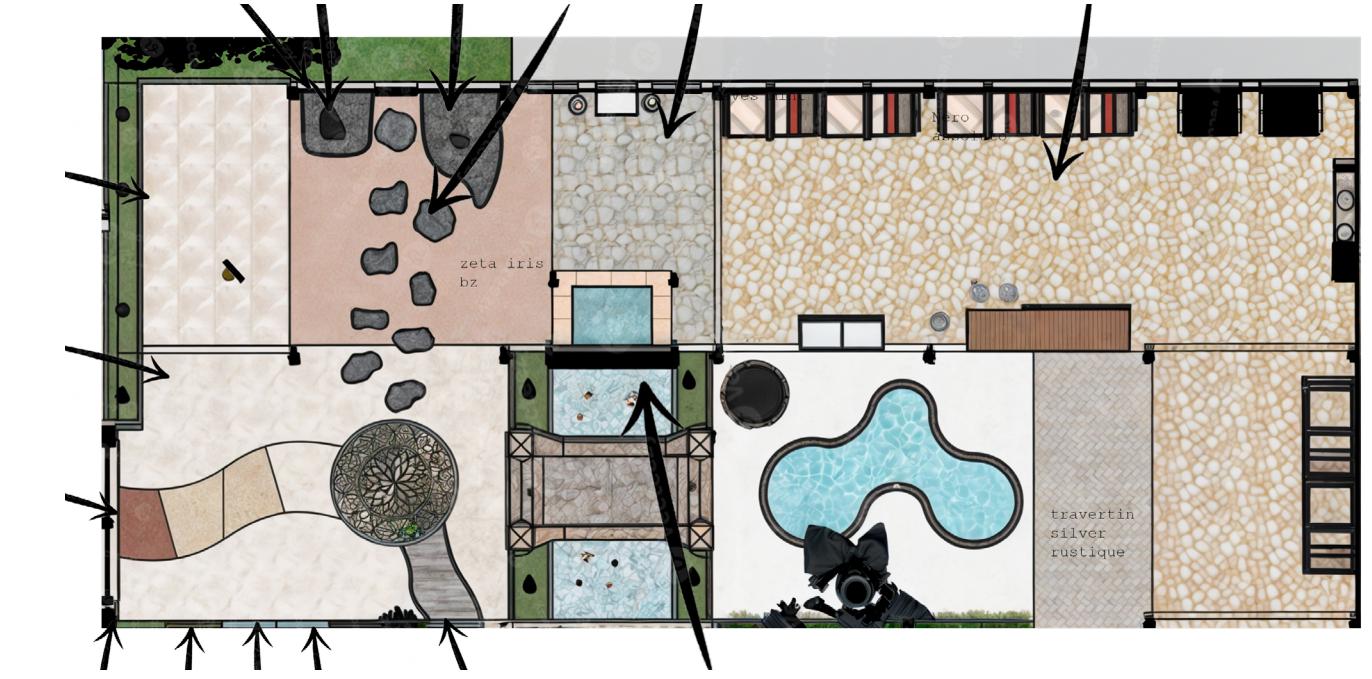



**BED**

Beltrando Enzo Design



**BED**  
Beltrando Enzo Design

## 04 Le Mas posant

Le projet "Le Mas Posant" consiste en la rénovation d'une maison traditionnelle transformée en maison de soins spécialisée pour les bébés. L'objectif principal a été de respecter scrupuleusement les normes en vigueur tout en répondant aux exigences et aux goûts spécifiques des clients. Chaque détail a été minutieusement pensé pour allier confort, sécurité et bien-être des petits résidents, tout en créant un espace apaisant et fonctionnel.




BED

Beltrando Enzo Design

Depuis sketchup 13



# Plan

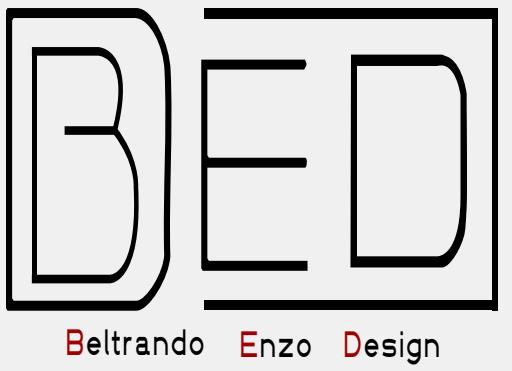

Projet  
548 Av. du Général de Gaulle





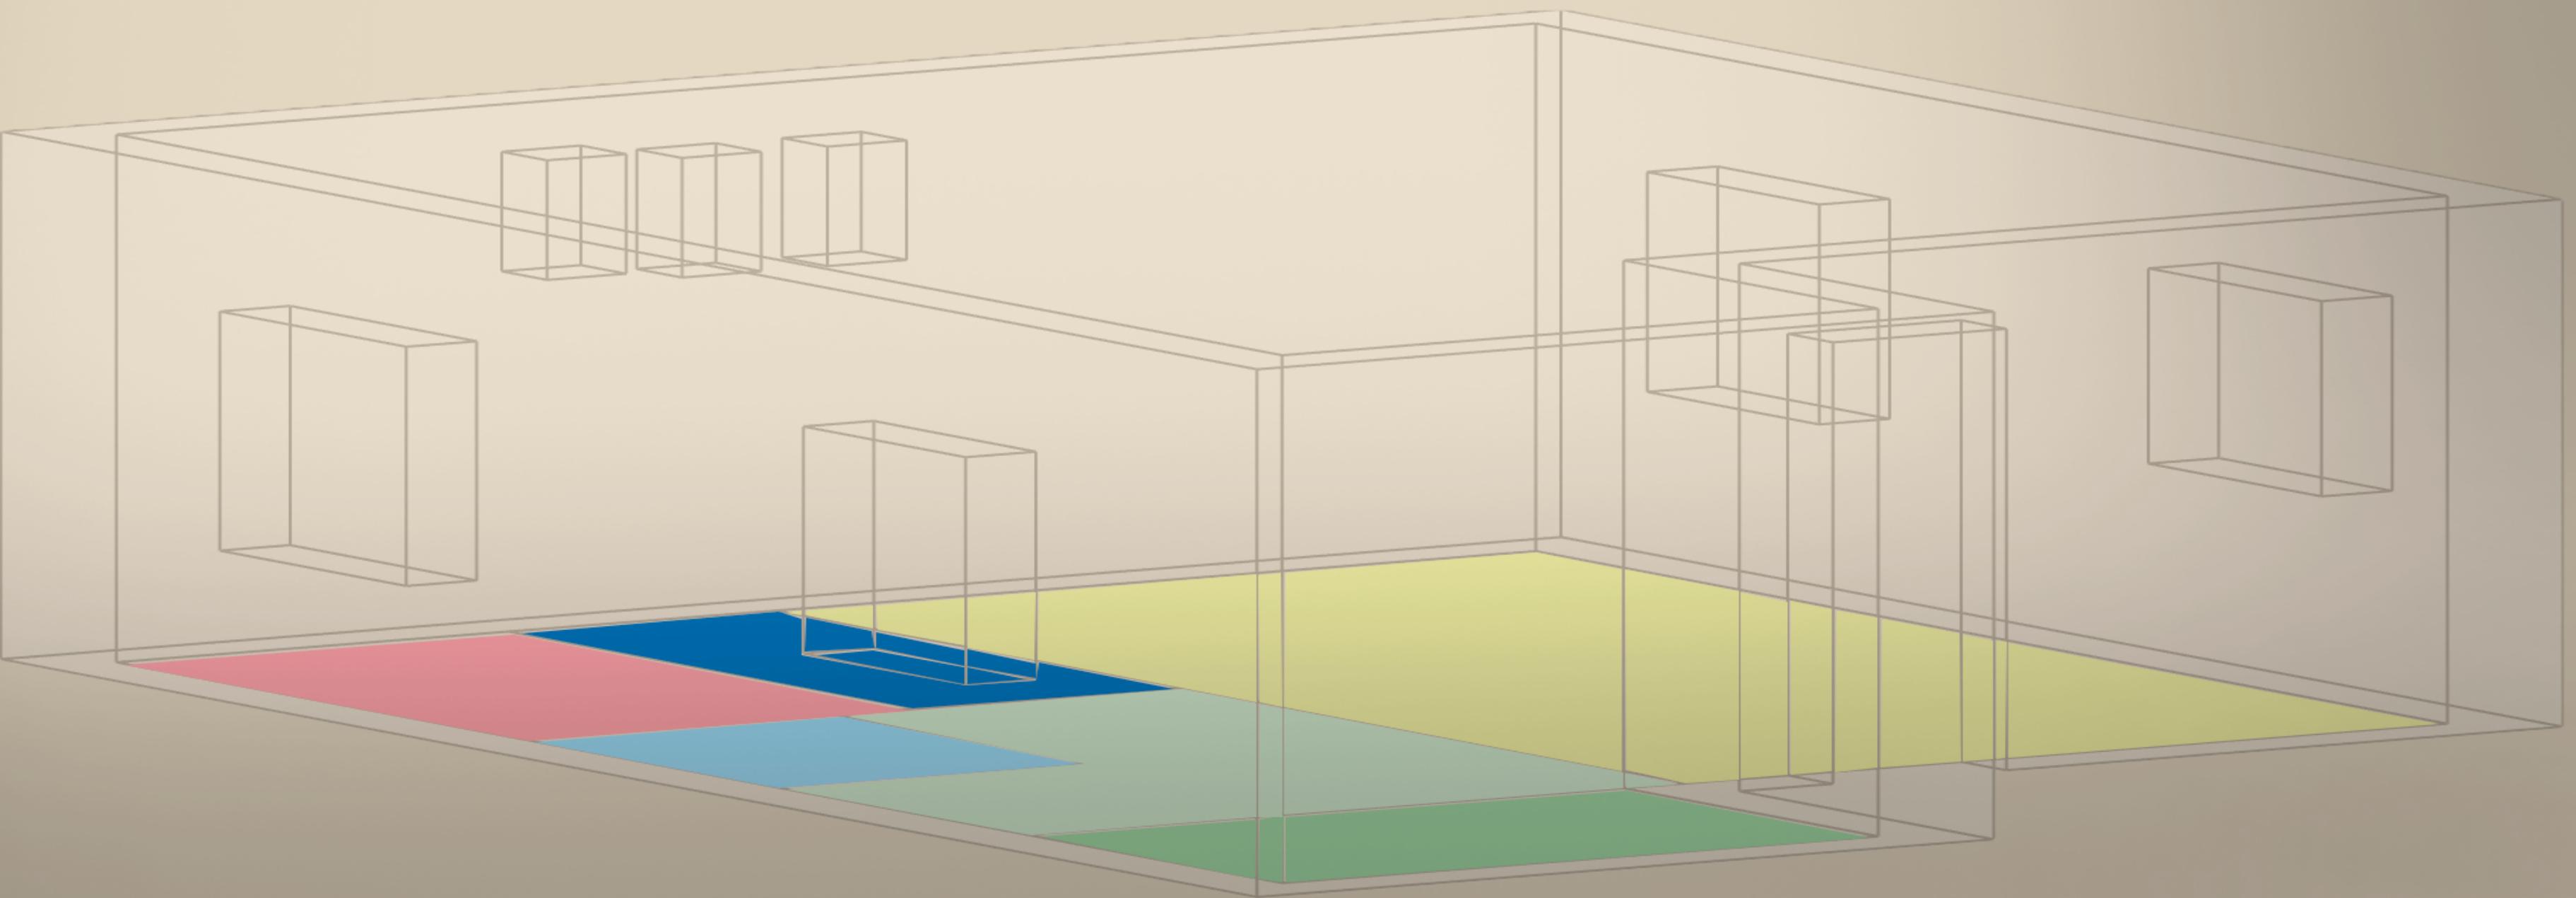
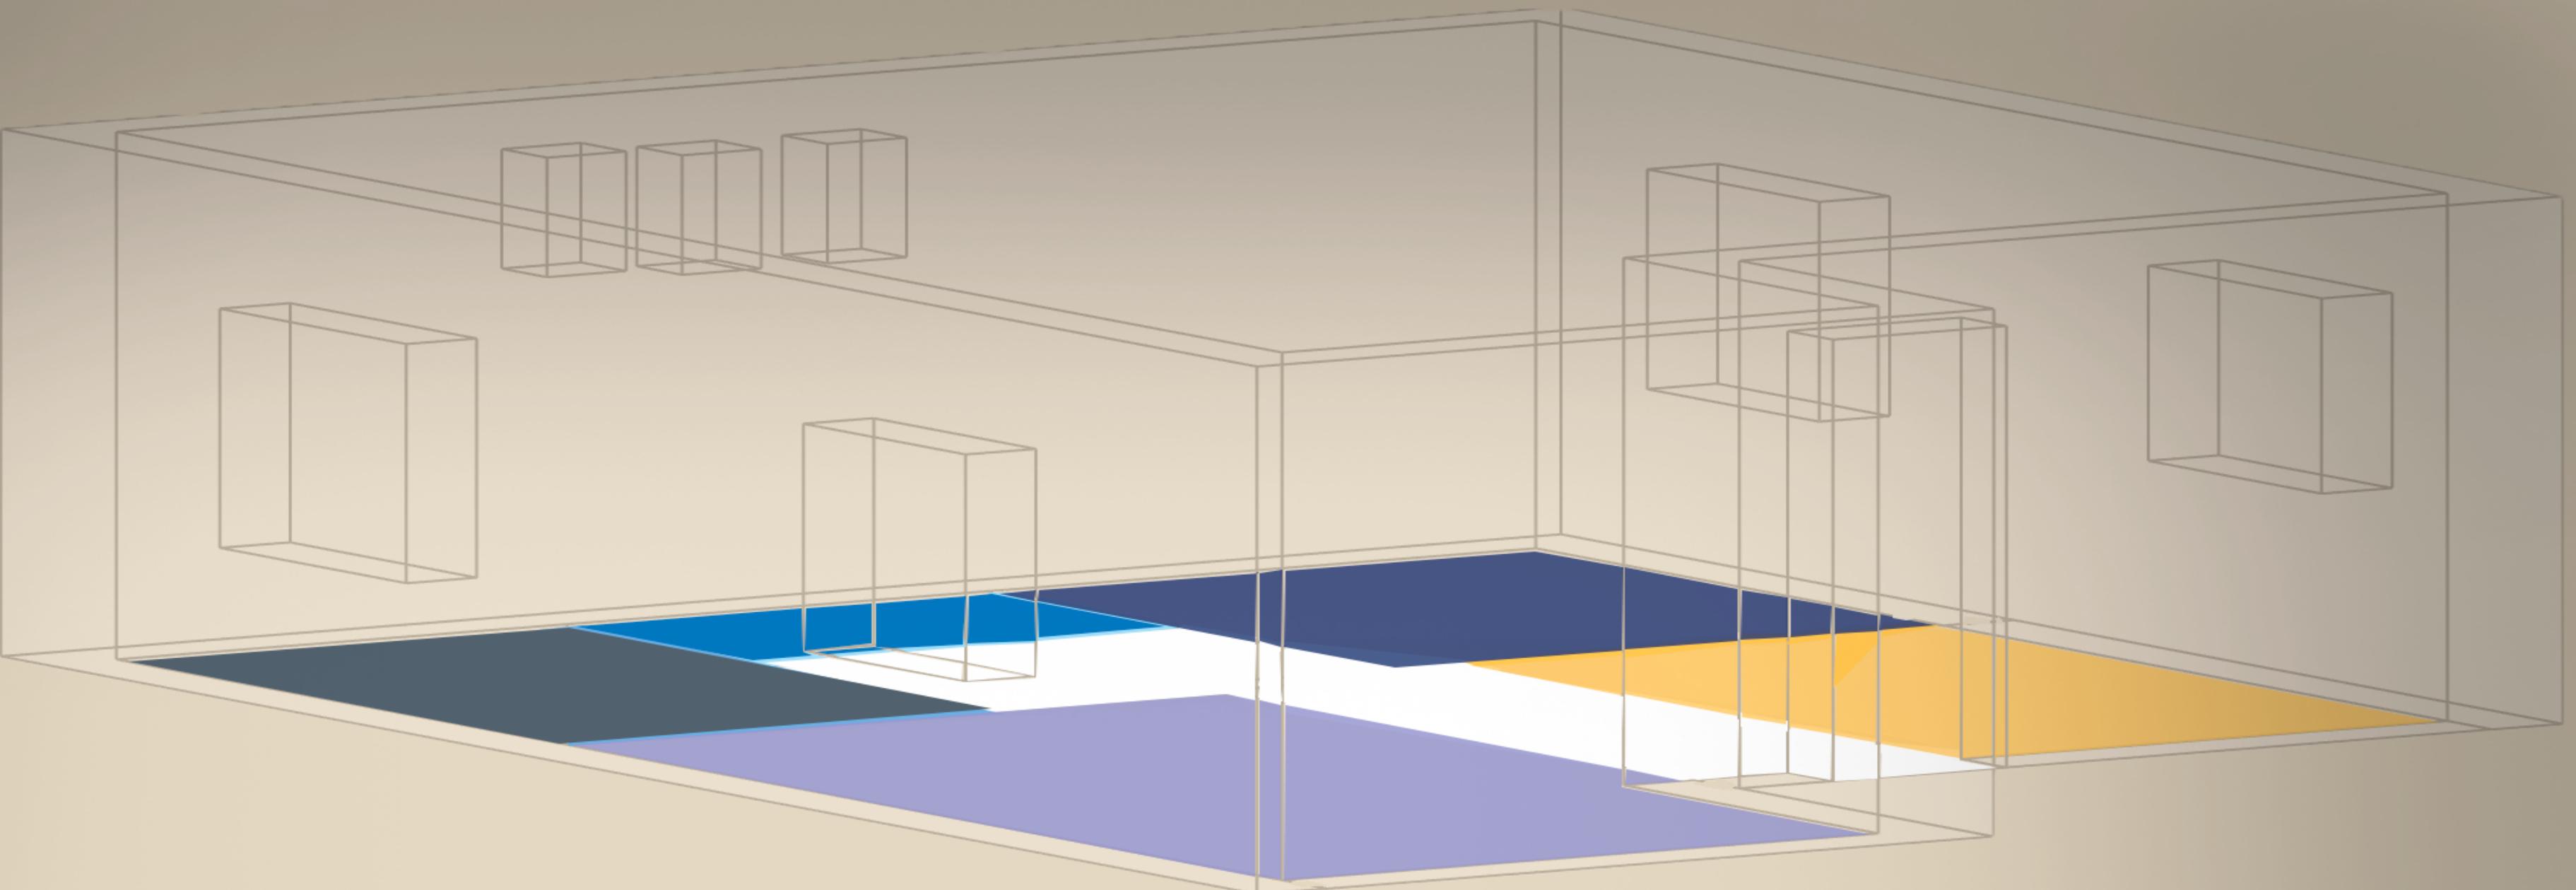




**BED**  
Beltrando Enzo Design

Coupe BB'

# "Less is more."

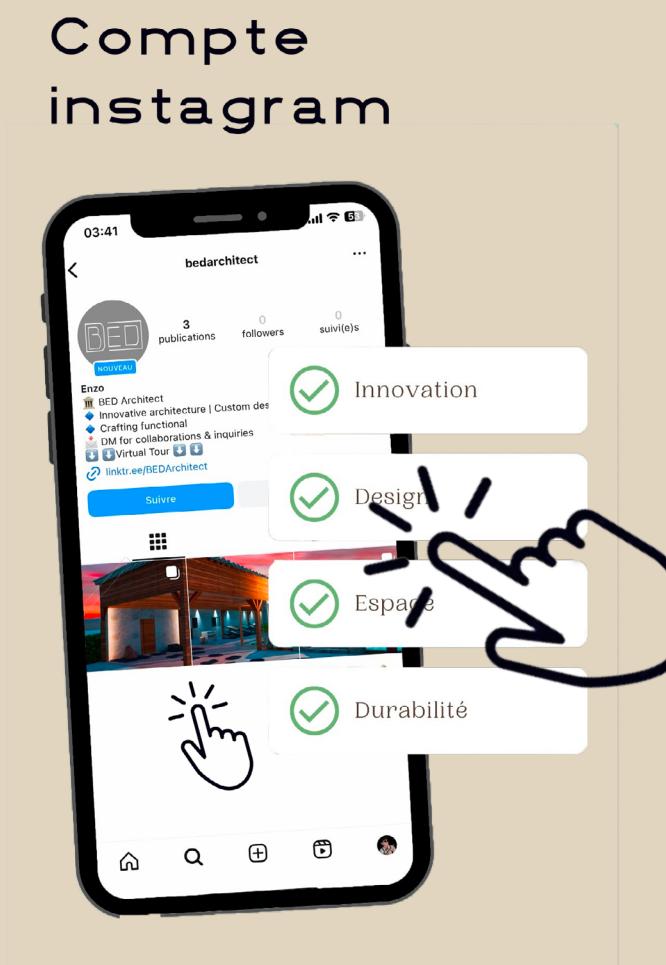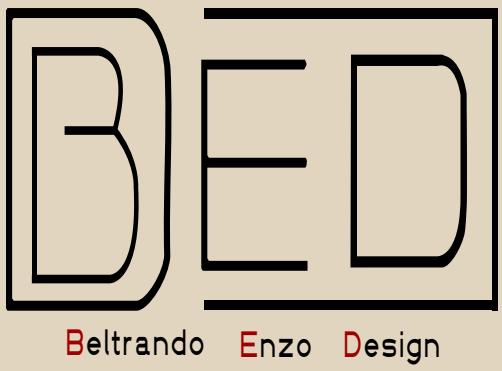

Contact: 06 88 98 96 90  
Mail: [bed.contact.me@gmail.com](mailto:bed.contact.me@gmail.com)